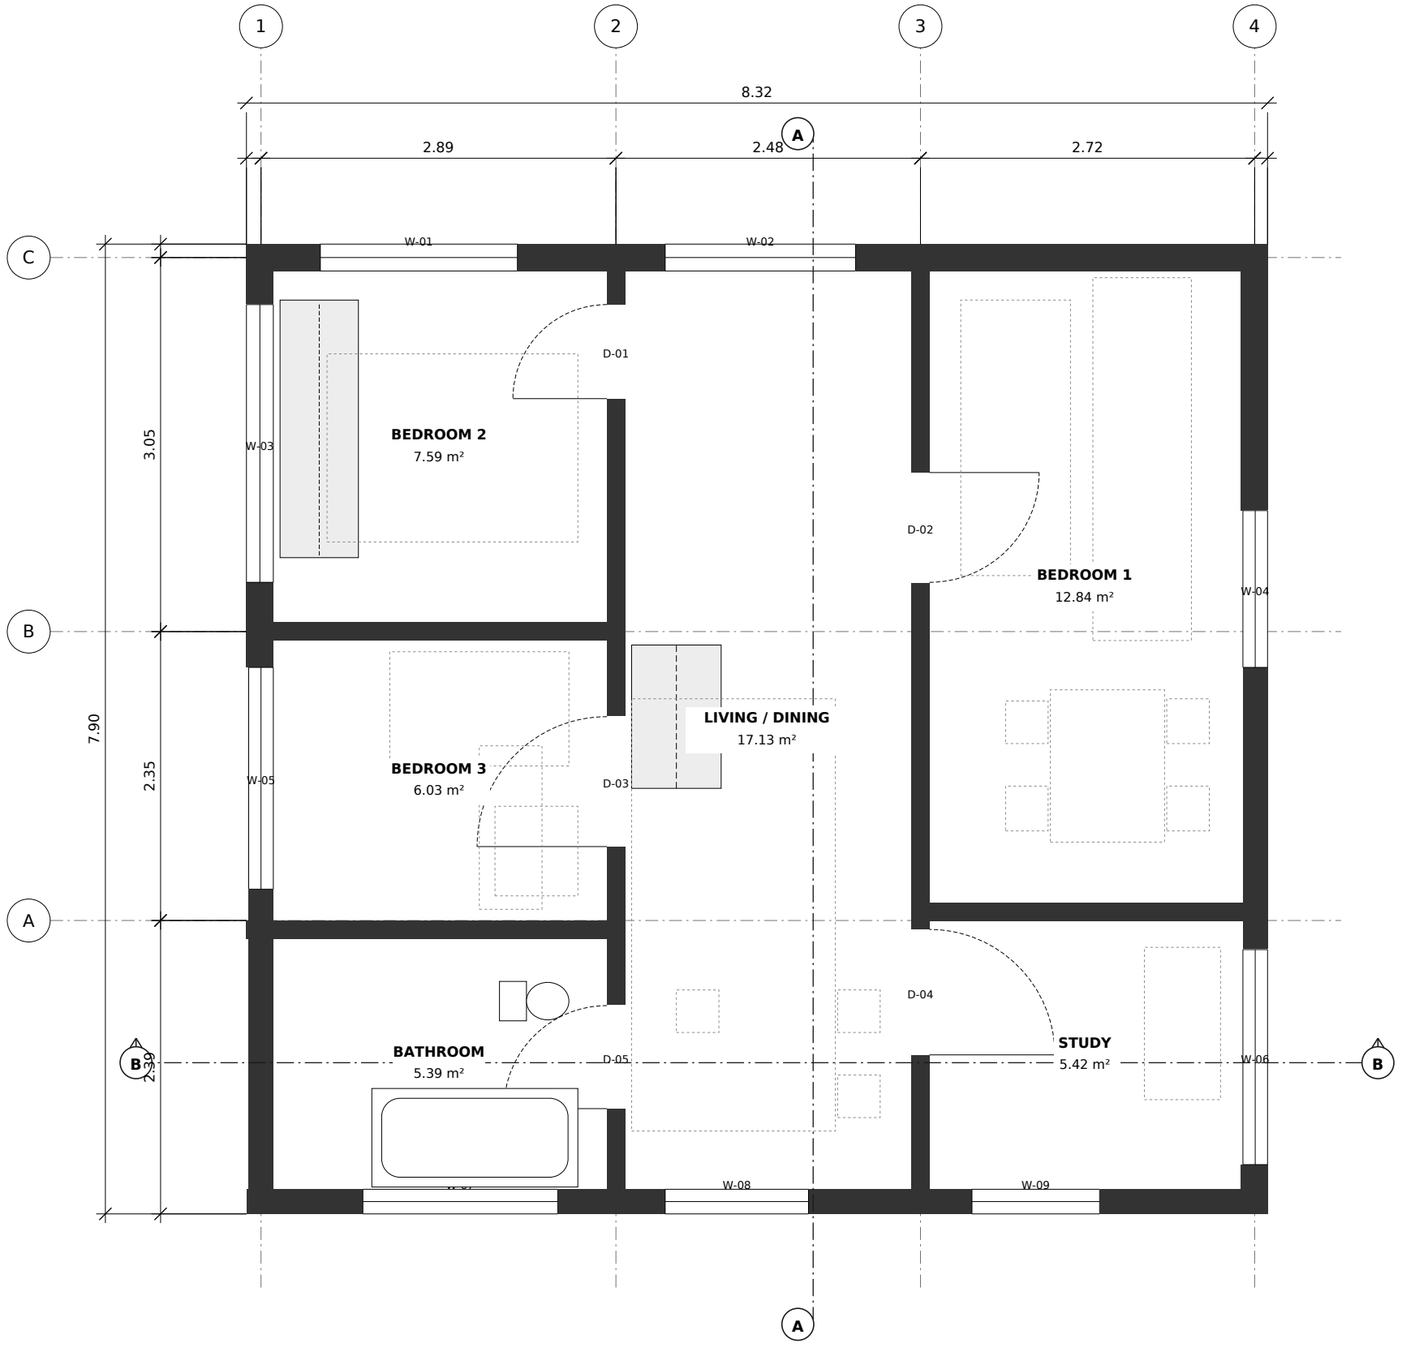


FLOOR PLAN — 1:50

Dimensions in metres, to wall axes. Finished state: fixed casework and fixtures shown; loose furniture dashed (indicative only).

0 1 2 3 4 5 m

ZERO MOUSE CLICKS

Floor plan set from a marketing image

NOTE

Drawn from marketing plan — verify dimensions on site. Marketing plans are not to scale; this set is scaled from the declared private area. Wall thicknesses and openings are approximate.

TITLE	**FLOOR PLAN**
PROJECT	Synthetic example
UNIT	Type 000
DECLARED PRIVATE AREA	54.4 m²
SCALE	1:50 (A3)
DATE	2026-11-11
DRAWN BY	Zero Mouse Clicks · rules engine
SHEET	**A-101 (1/6)**

AREA & FINISH SCHEDULE (m²)

Space	Use	Floor	Area	Share
S-01	BEDROOM 2	F1	7.59	14.0 %
S-02	LIVING / DINING	F1	17.13	31.5 %
S-03	BEDROOM 1	F3	12.84	23.6 %
S-04	BEDROOM 3	F3	6.03	11.1 %
S-05	STUDY	F1	5.42	10.0 %
S-06	BATHROOM	F2	5.39	9.9 %
TOTAL	net interior		54.40	100 %

Footprint (outer envelope): 8.32 x 7.90 m. Typical wall thickness ~14 cm.

DOOR & WINDOW SCHEDULE

Tag	Type	Width (m)	Height (m)
D-01	Door	0.77	2.10
D-02	Door	0.89	2.10
D-03	Door	1.06	2.10
D-04	Door	1.02	2.10
D-05	Door	0.84	2.10
W-01	Window	1.61	1.20 (assumed)
W-02	Window	1.55	1.20 (assumed)
W-03	Window	2.26	1.20 (assumed)
W-04	Window	1.28	1.20 (assumed)
W-05	Window	1.81	1.20 (assumed)
W-06	Window	1.75	1.20 (assumed)
W-07	Window	1.59	1.20 (assumed)
W-08	Window	1.17	1.20 (assumed)
W-09	Window	1.04	1.20 (assumed)

FIXTURES & CASEWORK

Item	Qty
BATHTUB	1
CLOSET	1
COUNTER	1
TOILET	1

ASSUMPTIONS

1. Scale derived from declared area (declared private area 54.4 m² = sum of net interior spaces).
2. Walls, doors and windows read from the image by a small on-device model and squared by rules.
3. Door heights 2.10 m and window heights 1.20 m are assumed; clear height 2.45 m assumed.
4. Room names are read from the labels printed on the plan when present; otherwise inferred by rules.
5. Electrical points (A-104) are a rule-based schematic proposal, not taken from the source plan.
6. Drawn from marketing plan — verify dimensions on site.

ZERO MOUSE CLICKS

Floor plan set from a marketing image

NOTE

Drawn from marketing plan —
verify dimensions on site.
Marketing plans are not to scale; this set is scaled from the declared private area. Wall thicknesses and openings are approximate.

TITLE
AREAS & OPENINGS SCHEDULES

PROJECT
Synthetic example

UNIT
Type 000


DECLARED PRIVATE AREA
54.4 m²

SCALE
n.t.s.

DATE
2026-11-11

DRAWN BY
Zero Mouse Clicks · rules engine

SHEET
A-102 (2/6)

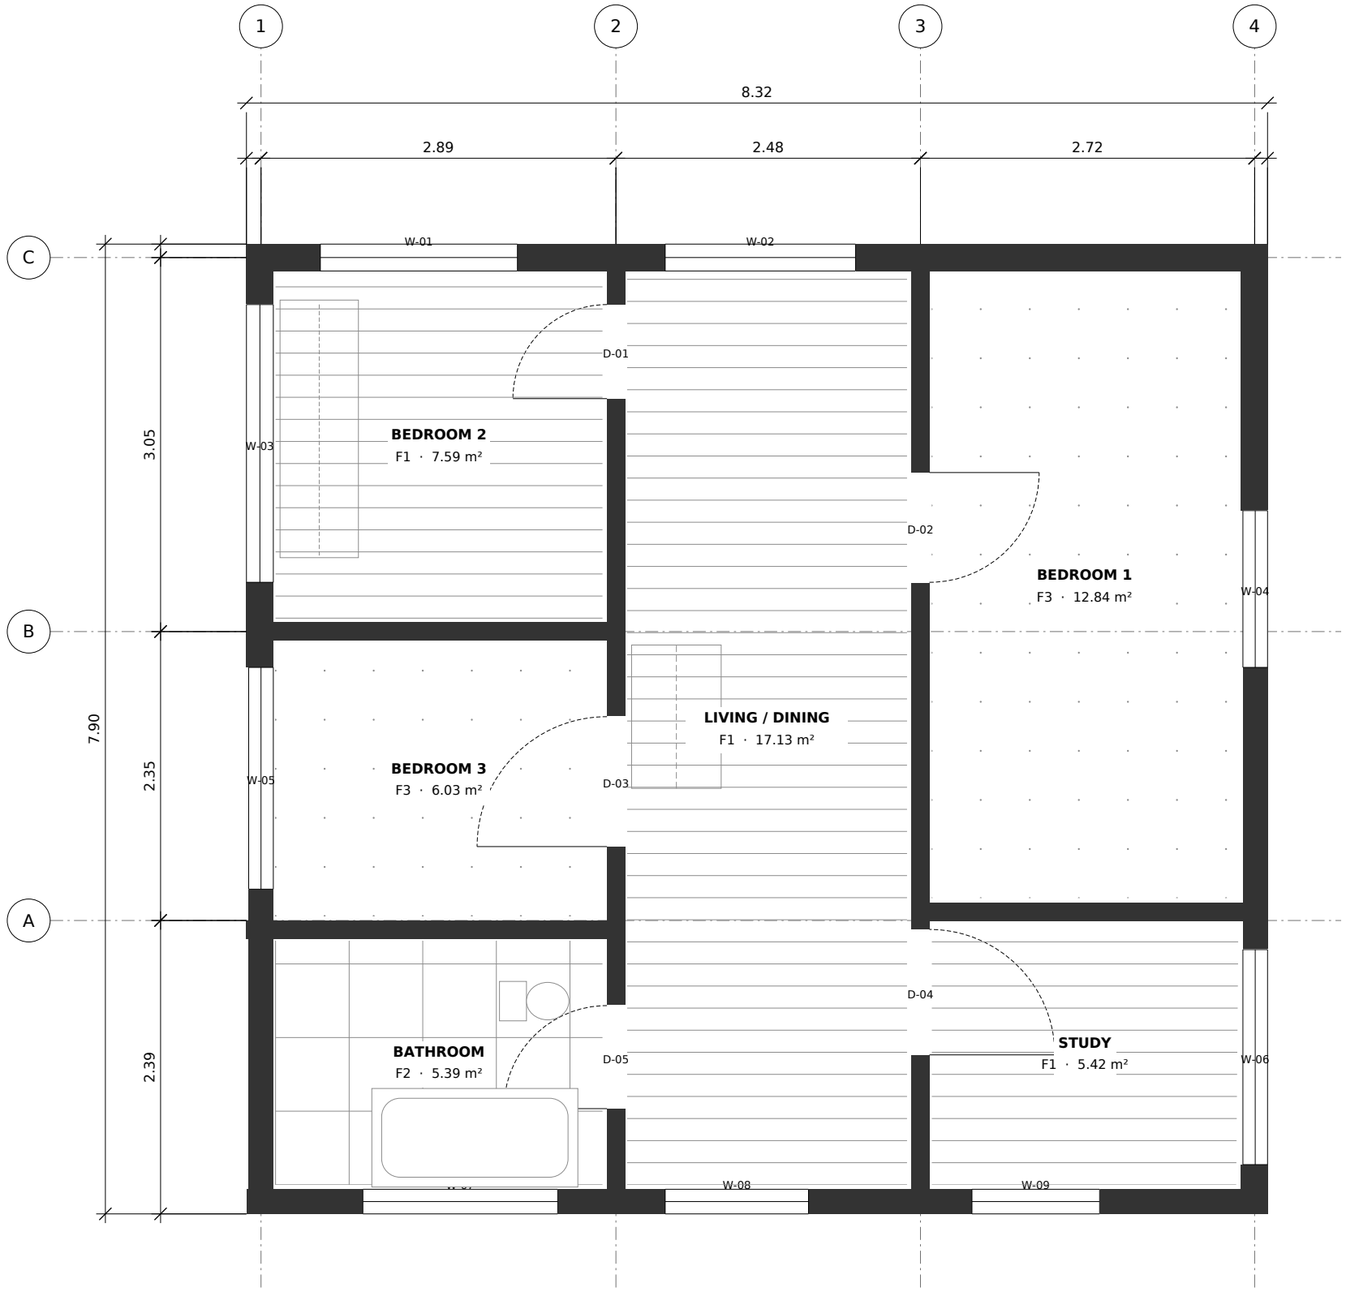

FLOOR FINISHES PLAN — 1:50

Dimensions in metres, to wall axes. Floor finishes read from the marketing image texture; confirm against the developer spec.

0 1 2 3 4 5 m

ZERO MOUSE CLICKS

Floor plan set from a marketing image


LEGEND

F1 Wood-look laminate / plank
F2 Ceramic tile 60 x 60
F3 Porcelain / smooth finish
F4 Exterior — lawn / paving

NOTE

Drawn from marketing plan — verify dimensions on site. Marketing plans are not to scale; this set is scaled from the declared private area. Wall thicknesses and openings are approximate.

TITLE	**FLOOR FINISHES PLAN**
PROJECT	Synthetic example
UNIT	Type 000
DECLARED PRIVATE AREA	54.4 m²
SCALE	1:50 (A3)
DATE	2026-11-11
DRAWN BY	Zero Mouse Clicks · rules engine
SHEET	**A-103 (3/6)**

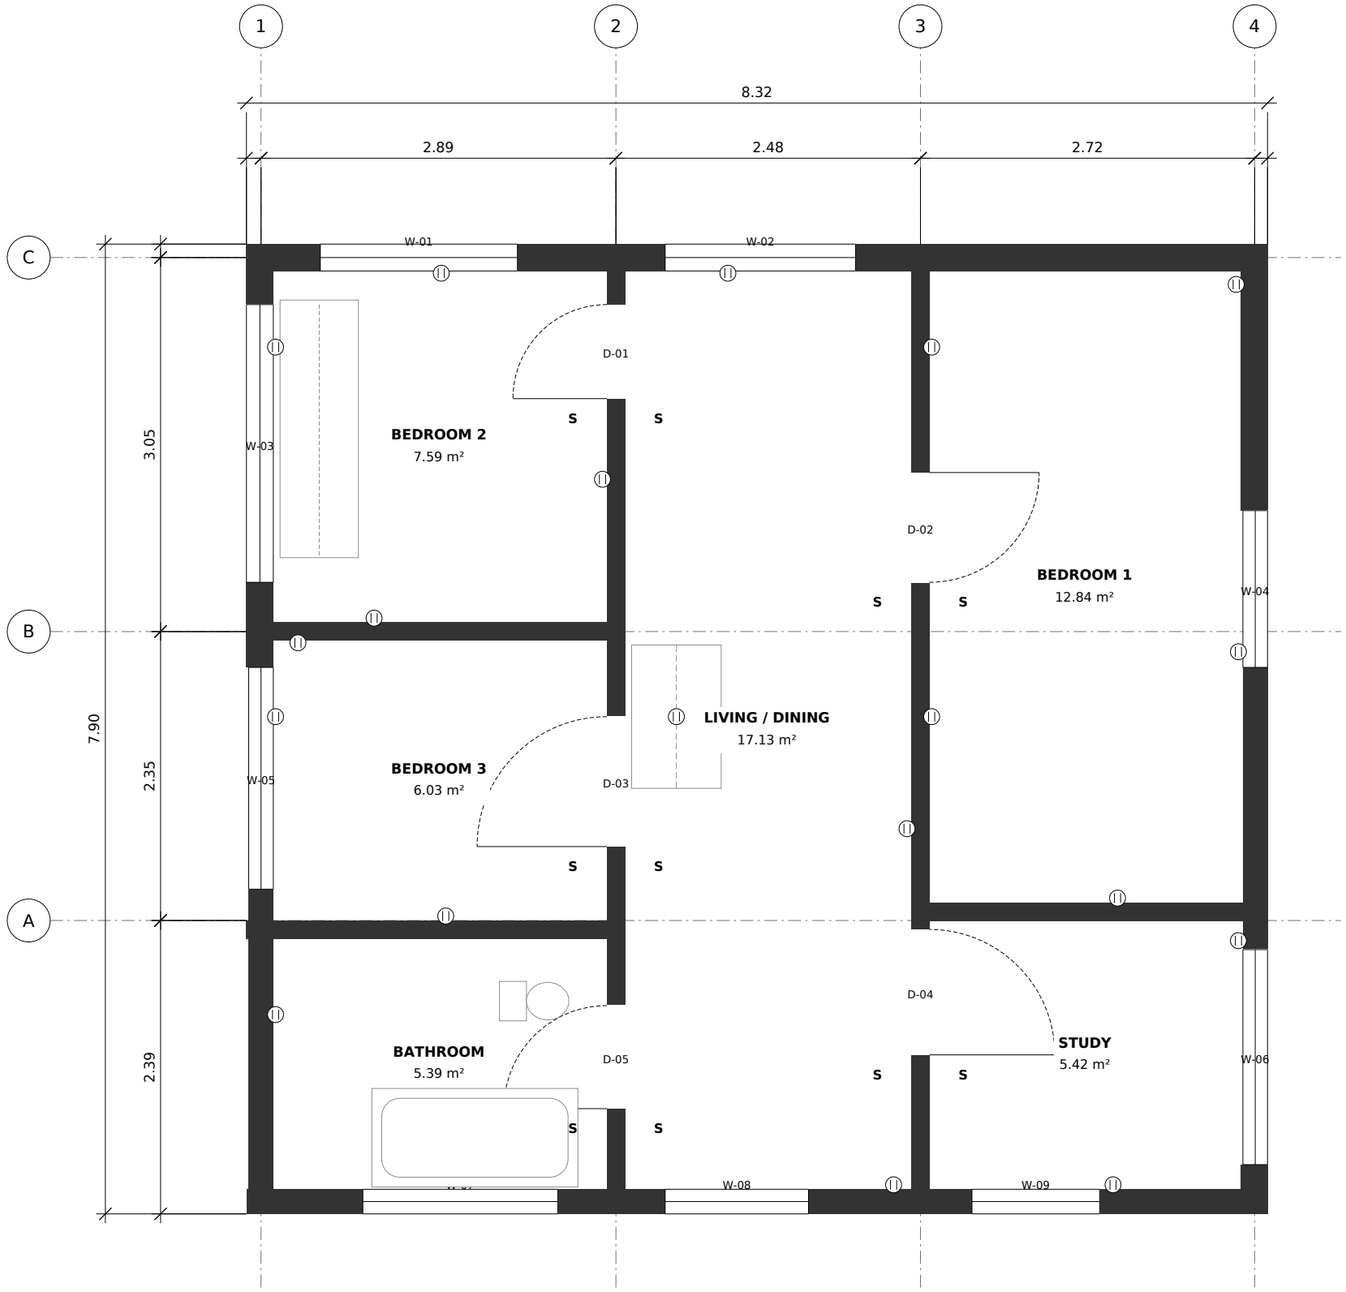

ELECTRICAL LAYOUT (SCHEMATIC) — 1:50

Dimensions in metres, to wall axes. SCHEMATIC PROPOSAL by rules — not in source plan. Verify with a licensed electrician / local code.

0 1 2 3 4 5 m

ZERO MOUSE CLICKS

Floor plan set from a marketing image

LEGEND

- Ceiling light point
- Duplex outlet (perimeter, ~3 m)
- GFCI GFCI outlet (counter ~1.2 m / lavatory)
- S Switch at door

NOTE

Drawn from marketing plan — verify dimensions on site. Marketing plans are not to scale; this set is scaled from the declared private area. Wall thicknesses and openings are approximate.

TITLE
ELECTRICAL LAYOUT (SCHEMATIC)

PROJECT
Synthetic example

UNIT
Type 000


DECLARED PRIVATE AREA
54.4 m²

SCALE
1:50 (A3)

DATE
2026-11-11

DRAWN BY
Zero Mouse Clicks · rules engine

SHEET
A-104 (4/6)

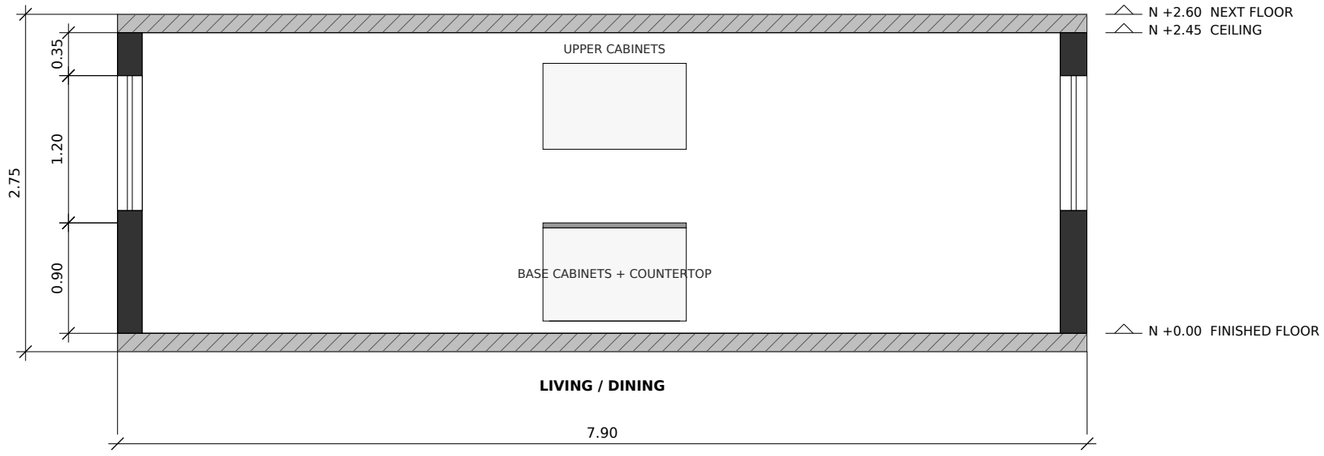

SECTION A-A (KITCHEN) — 1:50

Assumed: clear height 2.45 m, slab 0.15 m (floor-to-floor 2.60 m), doors 2.10 m, window sill 1.00 m (1.50 m in bathrooms), counter 0.90 m.
Schematic section derived from the plan; heights are standard assumptions — verify with the developer.

ZERO MOUSE CLICKS

Floor plan set from a marketing image

NOTE

Drawn from marketing plan — verify dimensions on site. Marketing plans are not to scale; this set is scaled from the declared private area. Wall thicknesses and openings are approximate.

TITLE
SECTION A-A (KITCHEN)

PROJECT
Synthetic example

UNIT
Type 000


DECLARED PRIVATE AREA
54.4 m²

SCALE
1:50 (A3)

DATE
2026-11-11

DRAWN BY
Zero Mouse Clicks · rules engine

SHEET
A-201 (5/6)

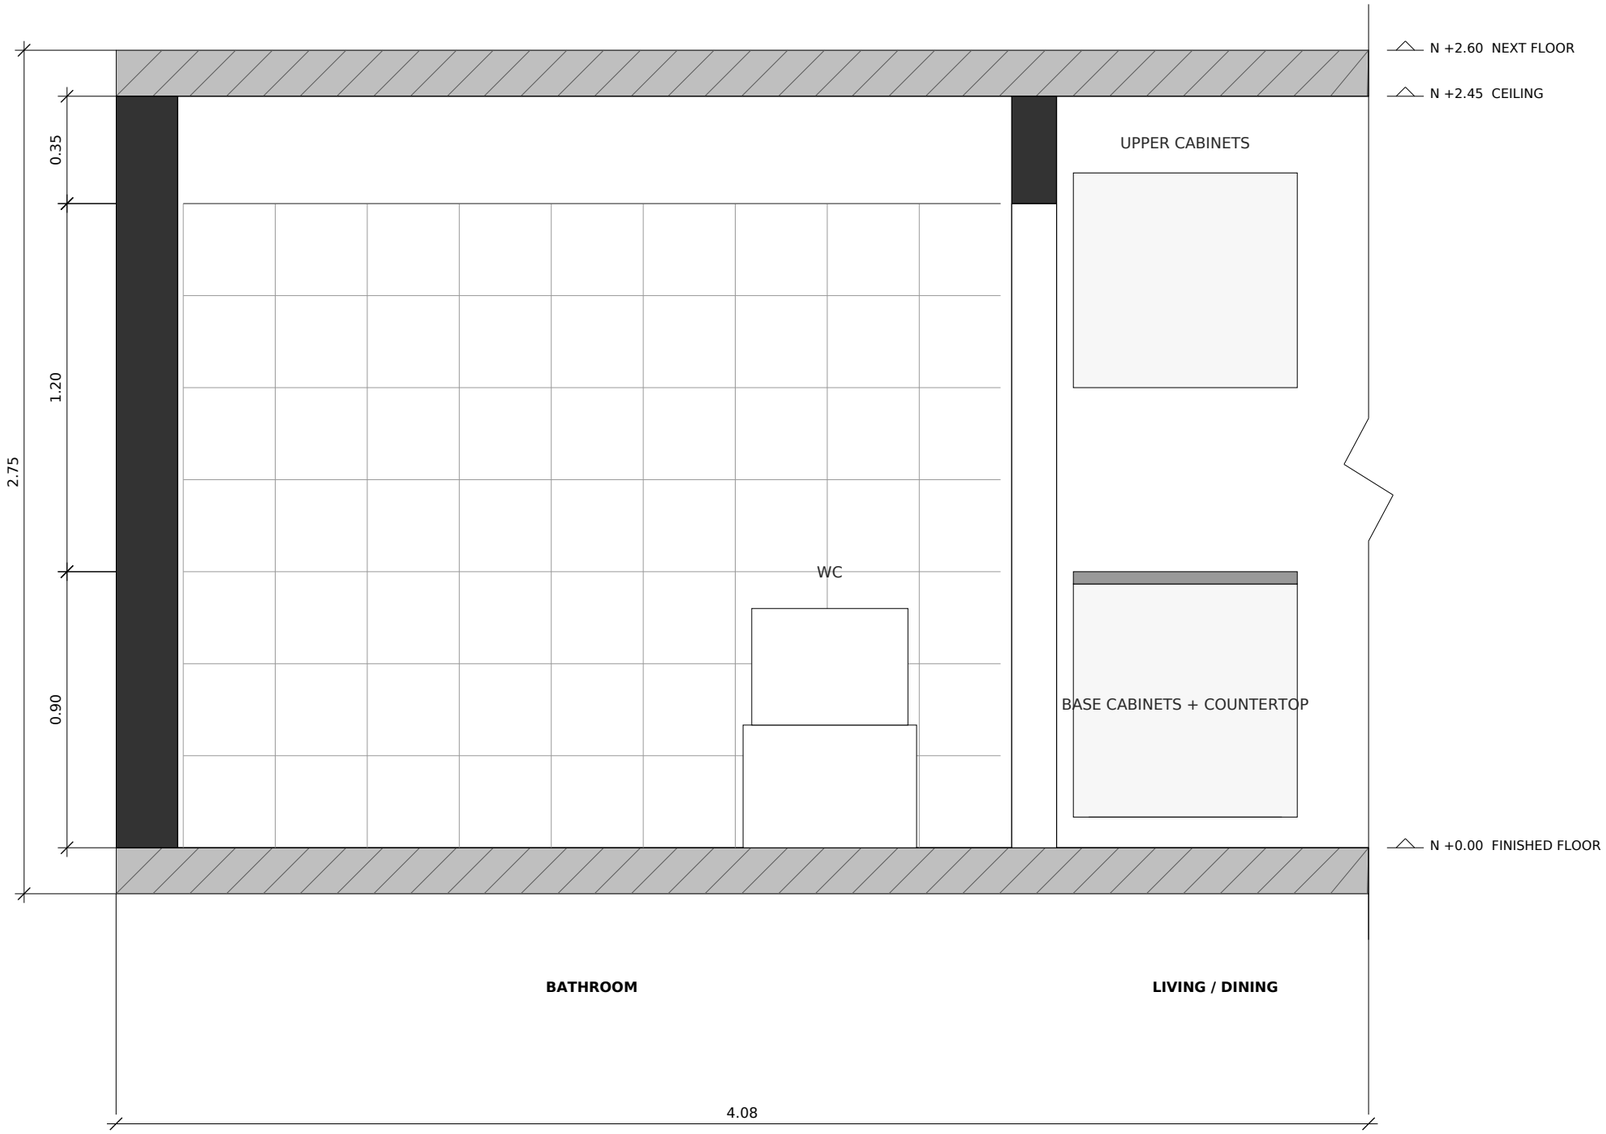

SECTION B-B (BATHROOM) — 1:20

Assumed: clear height 2.45 m, slab 0.15 m (floor-to-floor 2.60 m), doors 2.10 m, window sill 1.00 m (1.50 m in bathrooms), counter 0.90 m.
Schematic section derived from the plan; heights are standard assumptions — verify with the developer.

ZERO MOUSE CLICKS

Floor plan set from a marketing image

NOTE

Drawn from marketing plan —
verify dimensions on site.
Marketing plans are not to scale; this set is scaled from the declared private area. Wall thicknesses and openings are approximate.

TITLE	**SECTION B-B (BATHROOM)**
PROJECT	Synthetic example
UNIT	Type 000
DECLARED PRIVATE AREA	54.4 m²
SCALE	1:20 (A3)
DATE	2026-11-11
DRAWN BY	Zero Mouse Clicks · rules engine
SHEET	**A-202 (6/6)**